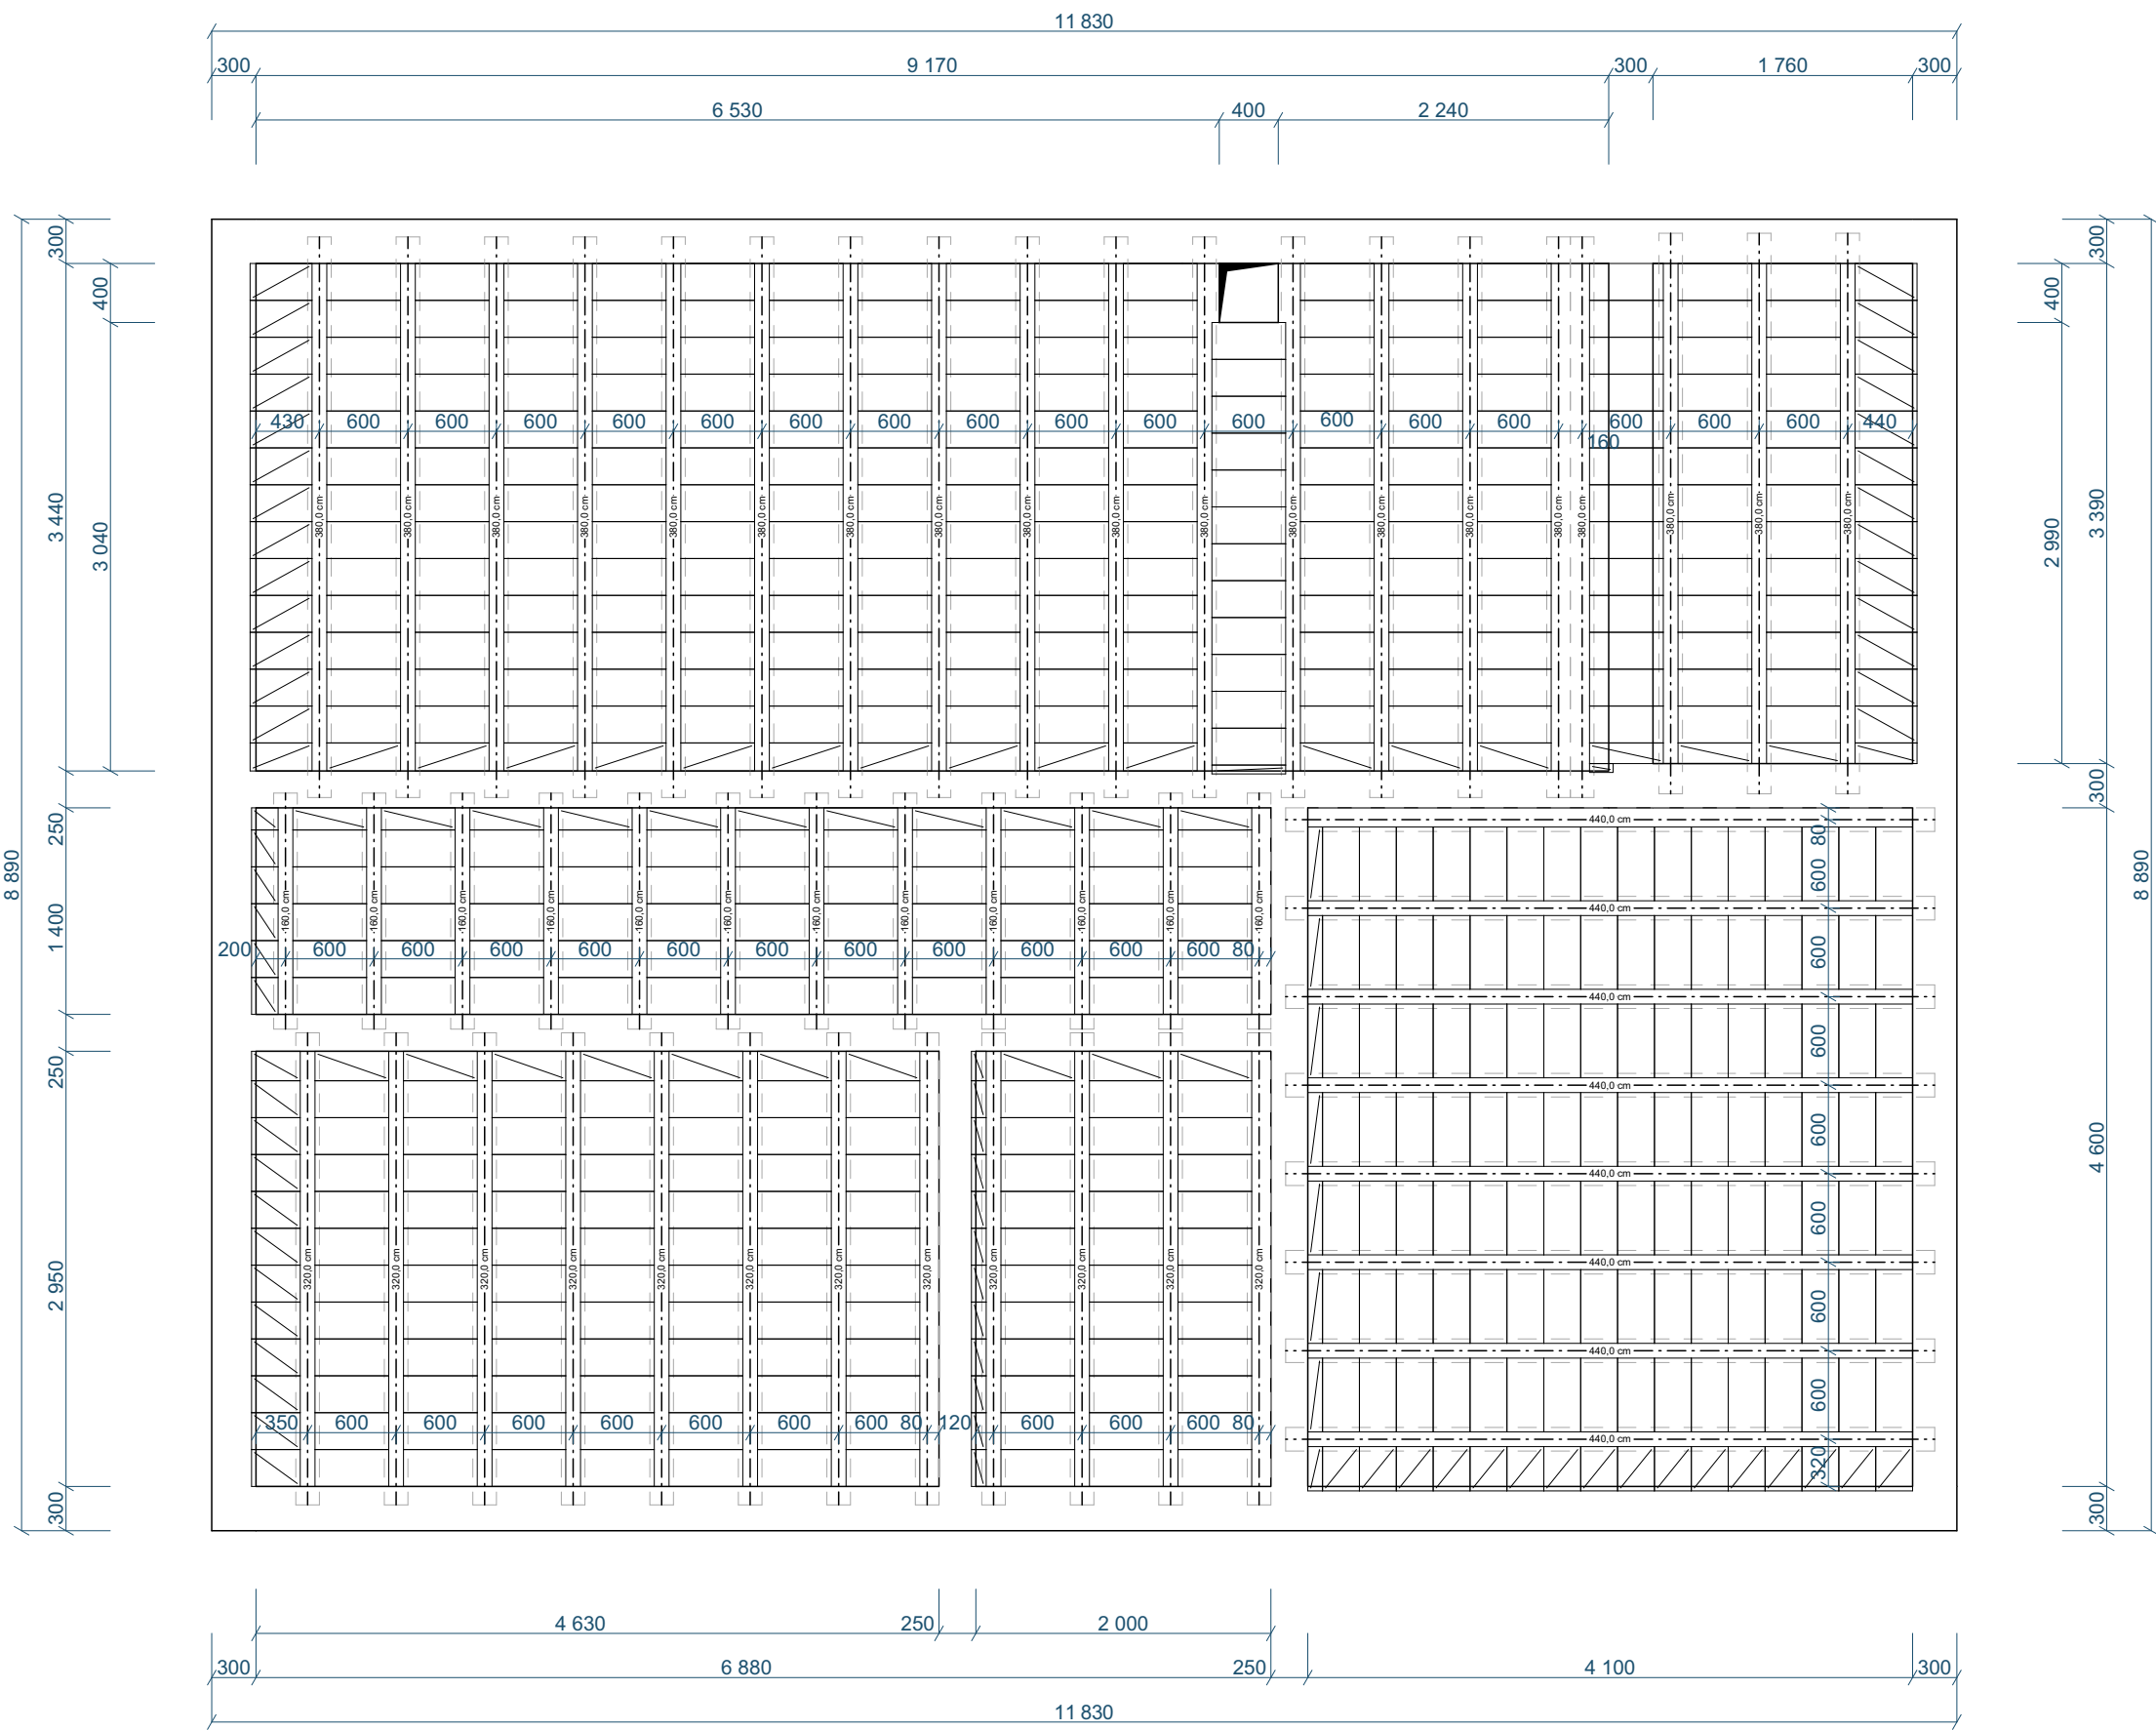


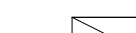
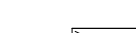
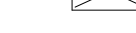
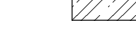
VÝKRES KLADENIA STROPU PORFIX NAD 2.NP



Výkaz stropných nosníkov		
Názov	Dĺžka (mm)	Počet (ks)
Stropný nosník PORFIX	1 600	12
Stropný nosník PORFIX	3 200	12
Stropný nosník PORFIX	3 800	19
Stropný nosník PORFIX	4 400	8

Výkaz stropných vložiek	
Názov	Počet (ks)
Stropná vložka PORFIX 500x200x250	607

LEGENDA:

-  Stropný nosník PORFIX
-  Stropná vložka PORFIX
-  Stropná vložka PORFIX - skrátená
-  Stropná vložka PORFIX - znížená o 1/2 rezaním
-  Monolitická časť
-  Otvor v stropnej konštrukcii (komin, výlez, schodisko a pod.)

POZNÁMKA:

- VÝSTUŽ VENCOV A ŽELEZOBETONOVÝCH KONŠTRUKCIÍ, AKO AJ POSÚDENIE ÚNOSNOSTI, NIE JE PREDMETOM RIEŠENIA KLADAČSKÉHO PLÁNU
- PRI REALIZÁCII STROPU JE BEZPODMIENEČNE NUTNÉ DODRŽAŤ MONTÁŽNY POSTUP A TECHNOLOGICKÝ NÁVOD NA ZABUDOVANIE PREDPÍSANÝ V PRODUKTOVÝCH LISTOCH A TECHNICKÝCH LISTOCH
- VRCHNÚ BETÓNOVÚ ZÁLIEVKU VYSTUŽIŤ ZVÁRANÝMI SIEŤAMI Ø6/200/200 ALEBO UKLADAŤ OCELOVÉ PRÚTY S PRIEMEROM 6 MM VO VZDIALENOSTI 200 MM A UPEVNIŤ DRÔTOM K POZDĹŽNÝM PRÚTOM NOSNÍKA.
- STROPNÉ VLOŽKY PRED BETONÁŽOU NAVLHČIŤ VODOU 4 - 6 L/M2
- BETÓN NA ZALIEVANIE MEDZIER MEDZI STROPNÝMI VLOŽKAMI A BETÓNOVÁ DOSKA S HRúbKOU 50 MM ZALIAŤ V JEDNEJ VRSTVE (spotreba betónu cca 0,09 - 010 m3/m2 vrátane venca)
- STROPNÉ NOSNÍKY PODOPRITE VO VZDIALENOSTI MAX. 1600 MM PODPERAMI - TRÁMAMI
- DO NOSNÍKOV DĹŽOK OD 5 M DO 6,6 M JE ODPORÚČANÉ VYKONAŤ UPROSTRED ROZPÄTIA PRIEČNE STUŽUJÚCE REBRO ŠÍRKY 250 MM A VÝŠKY 150 MM (VLOŽKA SA OREŽE PO VÝŠKE NA 100 MM)
- S VLOŽENOU VÝSTUŽOU 2× S PRIEMEROM 10 MM
- DO NOSNÍKOV DĹŽOK OD 6,8 M DO 8 M JE ODPORÚČANÉ VYKONAŤ V TRETINÁCH ROZPÄTIA 2× PRIEČNE STUŽUJÚCE REBRO ŠÍRKY 250 MM A VÝŠKY 150 MM (VLOŽKA SA OREŽE PO VÝŠKE NA 100 MM) S VLOŽENOU VÝSTUŽOU 2× S PRIEMEROM 10 MM

- ŠTANDARDNÁ VÝŠKA NADBETONÁVKY NAD VLOŽKAMI 50 MM, CELKOM HR. STROPU 250 MM
- HMOTNOSŤ STROPU BEZ BETÓNOVEJ ZÁLIEVKY JE 145 KG/M2.
- OSOVÁ VZDIALENOSŤ NOSNÍKOV JE 600 MM.

- STROPNÝ SYSTÉM PORFIX JE NAVRHNUTÝ PRE PREMENNÉ ZAŤAŽENIE KATEGÓRIE „A“ – OBYTNÉ PRIESTORY DO 2,0 KN/M2 (V ZMYSLE EN 15 037-1 BETÓNOVÉ PREFABRIKÁTY. MONTOVANÉ STROPY Z NOSNÍKOV A VLOŽIEK).

UPOZORNENIE!!!

TABUĽKY POUŽITIA STROPNÝCH NOSNÍKOV MAJÚ LEN INFORMATÍVNY CHARAKTER A NENAHRÁDZAJÚ STATICKÝ VÝPOČET, KTORÝ JE PRE UVEDENÉ KONŠTRUKCIE NUTNÝ. JEDNÁ SA O VODOROVNÚ NOSNÚ STAVEBNÚ KONŠTRUKCIU, KTORÁ PODLIEHA INDIVIDUÁLNEMU STATICKÉMU POSÚDENIU A DIMENZOVANIU. PORFIX - PÓROBETÓN, A.S. NENESIE ZODPOVEDNOSŤ ZA PRÍPADNÉ ŠKODY, KTORÉ VZNIKNÚ NEODBORNOU APLIKÁCIOU.

- **PRI ZÁVÄZNOM OBJEDNANÍ STROPNÉHO SYSTÉMU PONÚKAME MOŽNOSŤ BEZPLATNÉHO POSÚDENIA STATIKOM**

UVAŽOVANÉ MATERIÁLY

Betón C20/25

Výstuž prútov Bst500, B500

Horná výstuž nosníkov: ø8

VYPRACOVAL: Martin Vlha		
INVESTOR: Tomáš Žilka		
KÓD ZÁKAZNÍKA: SK26158397	MIESTO STAVBY: Zubrohlava	DÁTUM: 14. 4. 2026
Kladačský plán stropu PORFIX		