



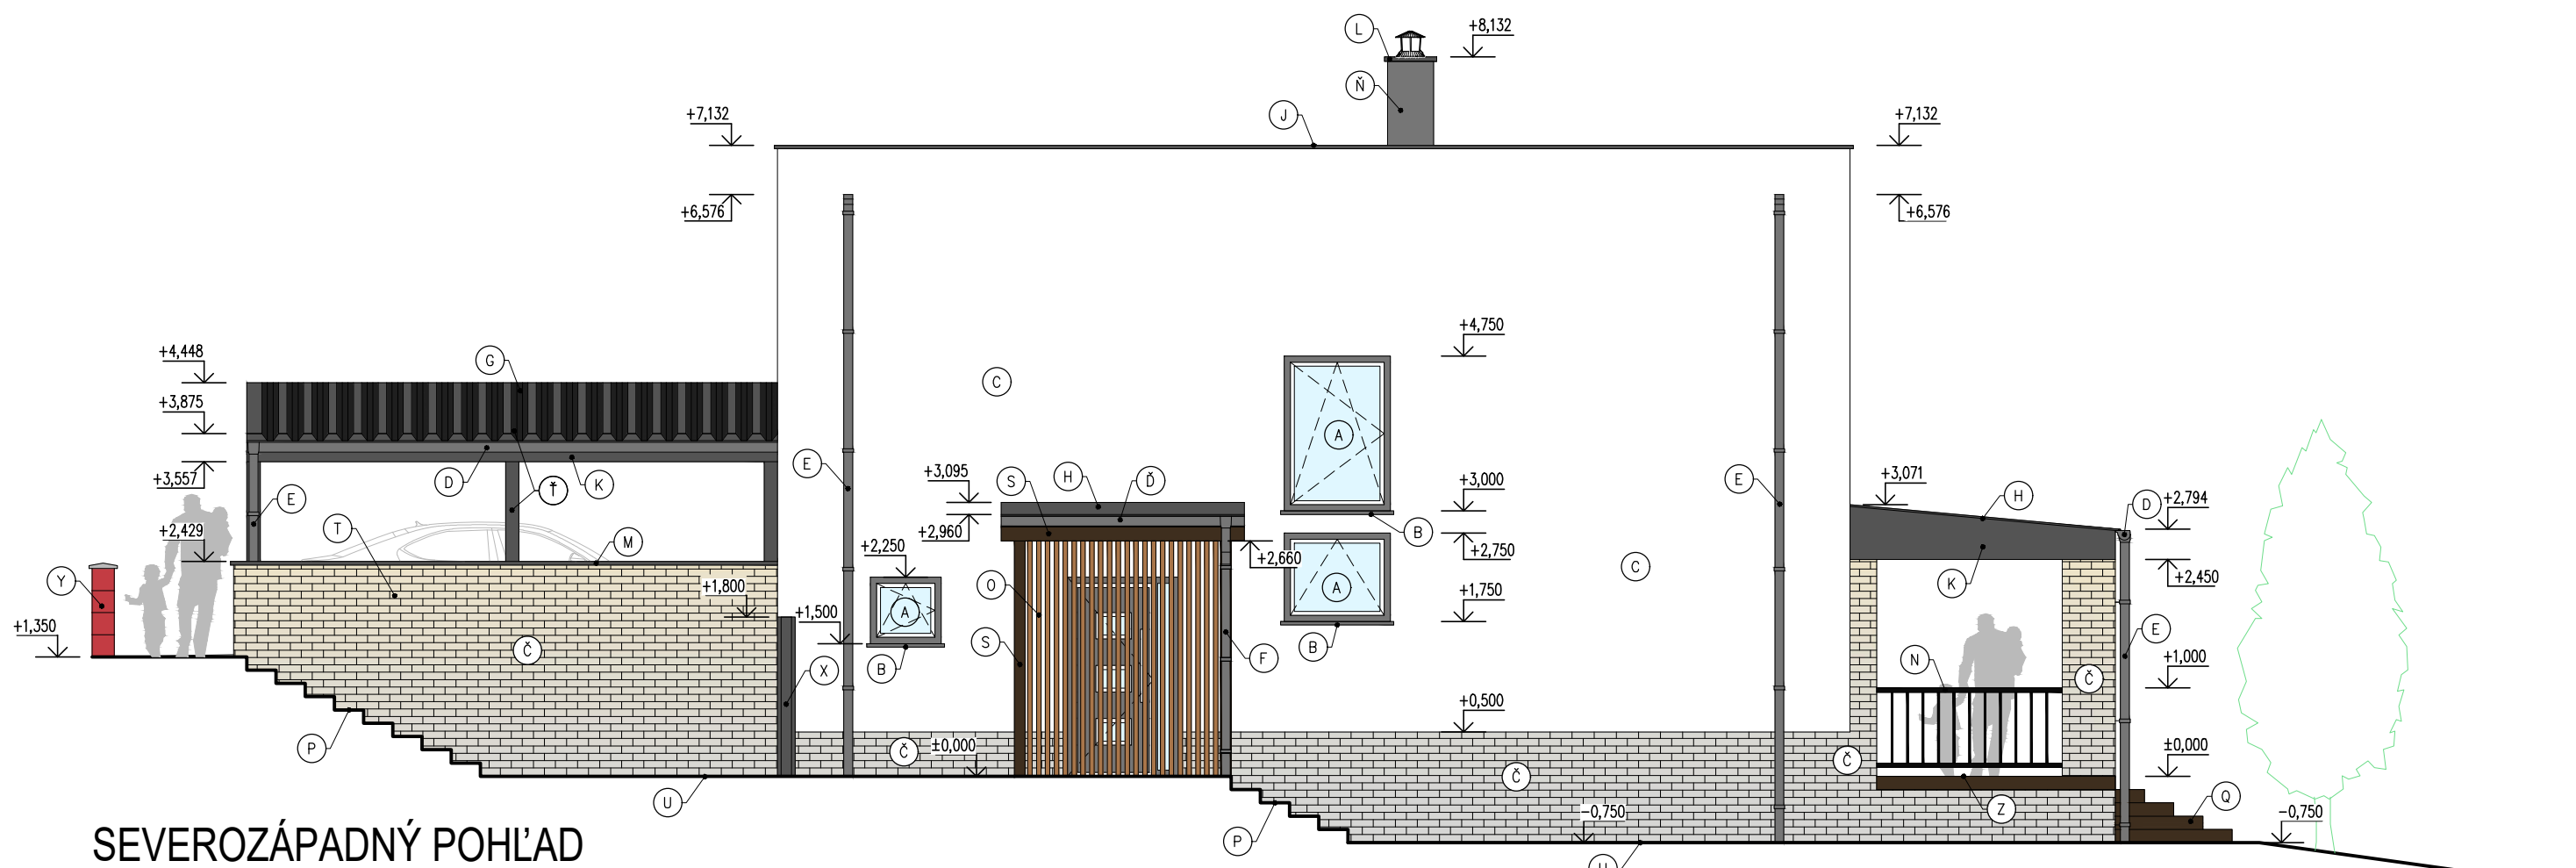


SEVEROZÁPADNÝ POHĽAD

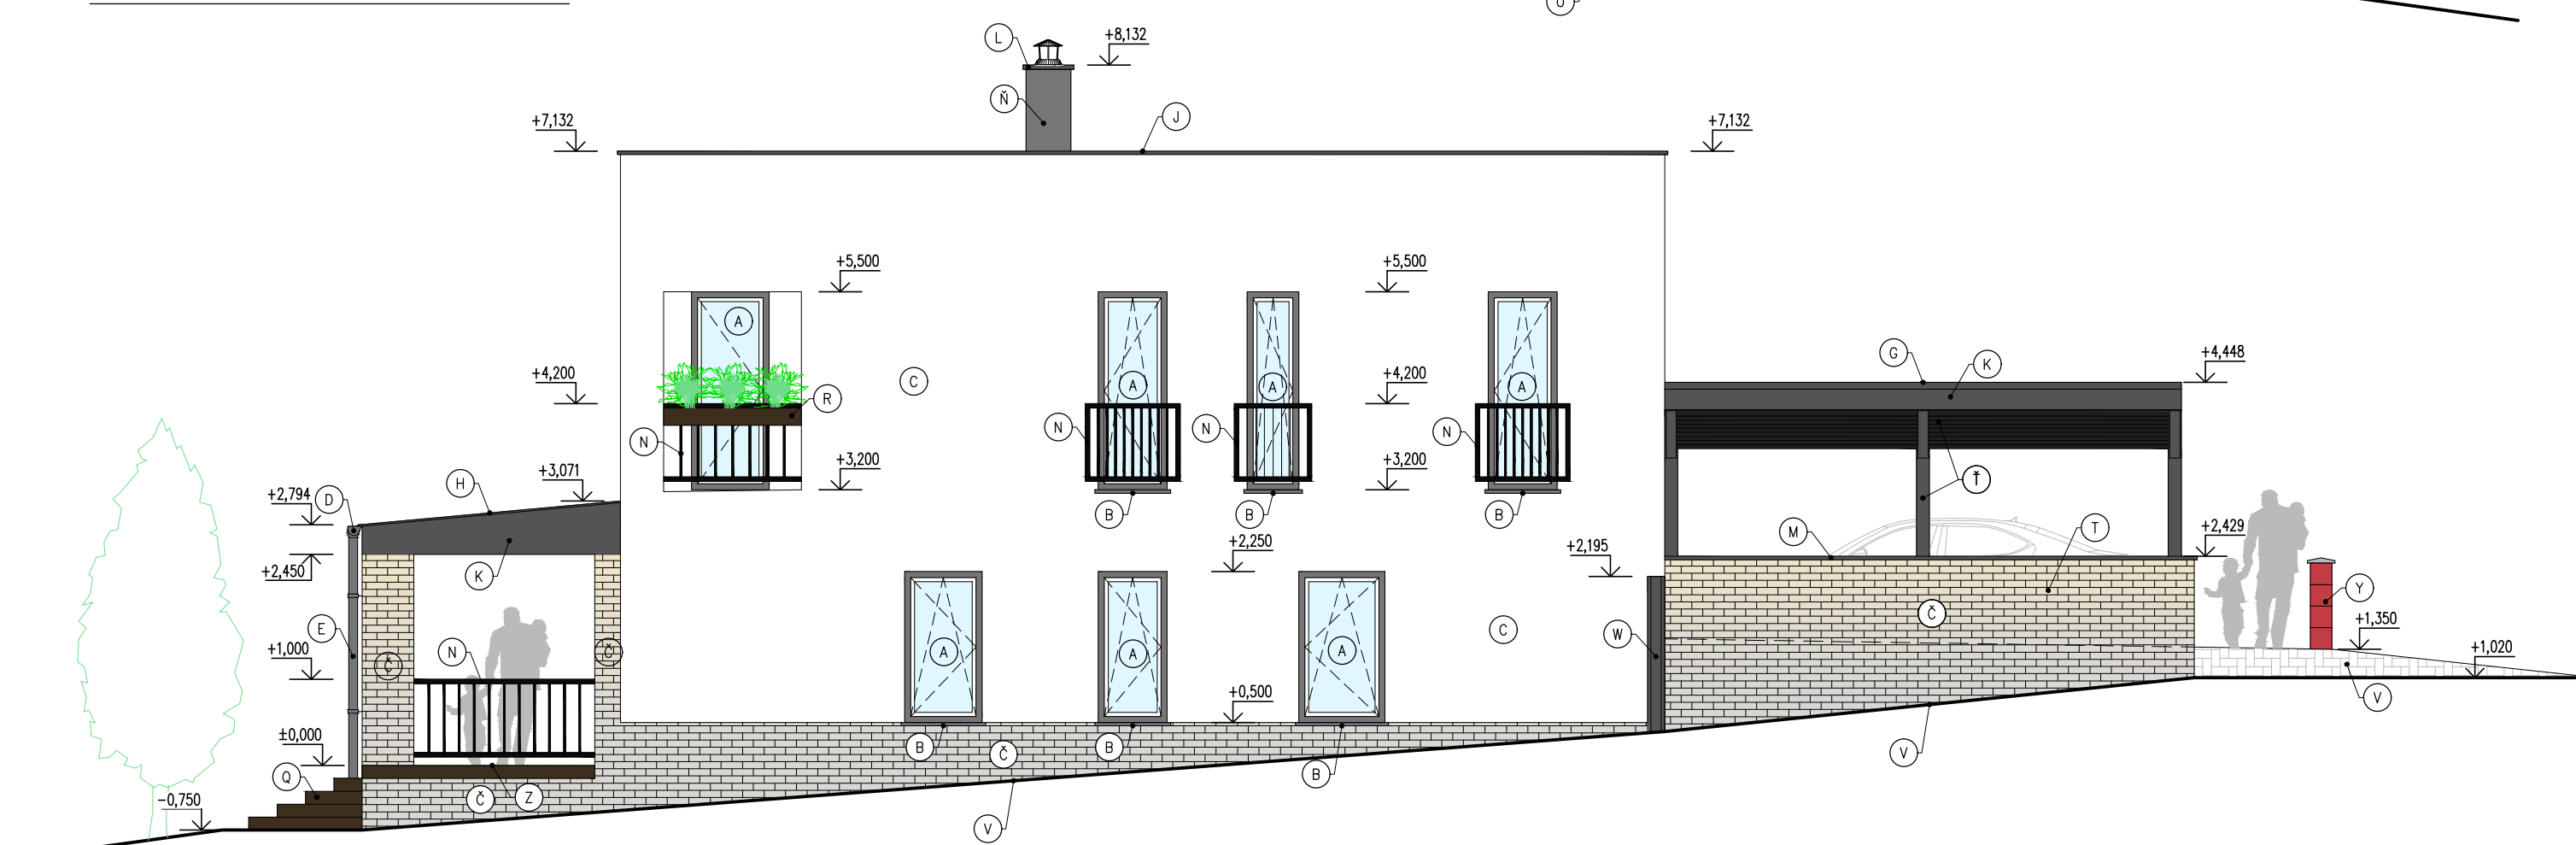

JUHOVÝCHODNÝ POHĽAD



JUHOZÁPADNÝ POHĽAD

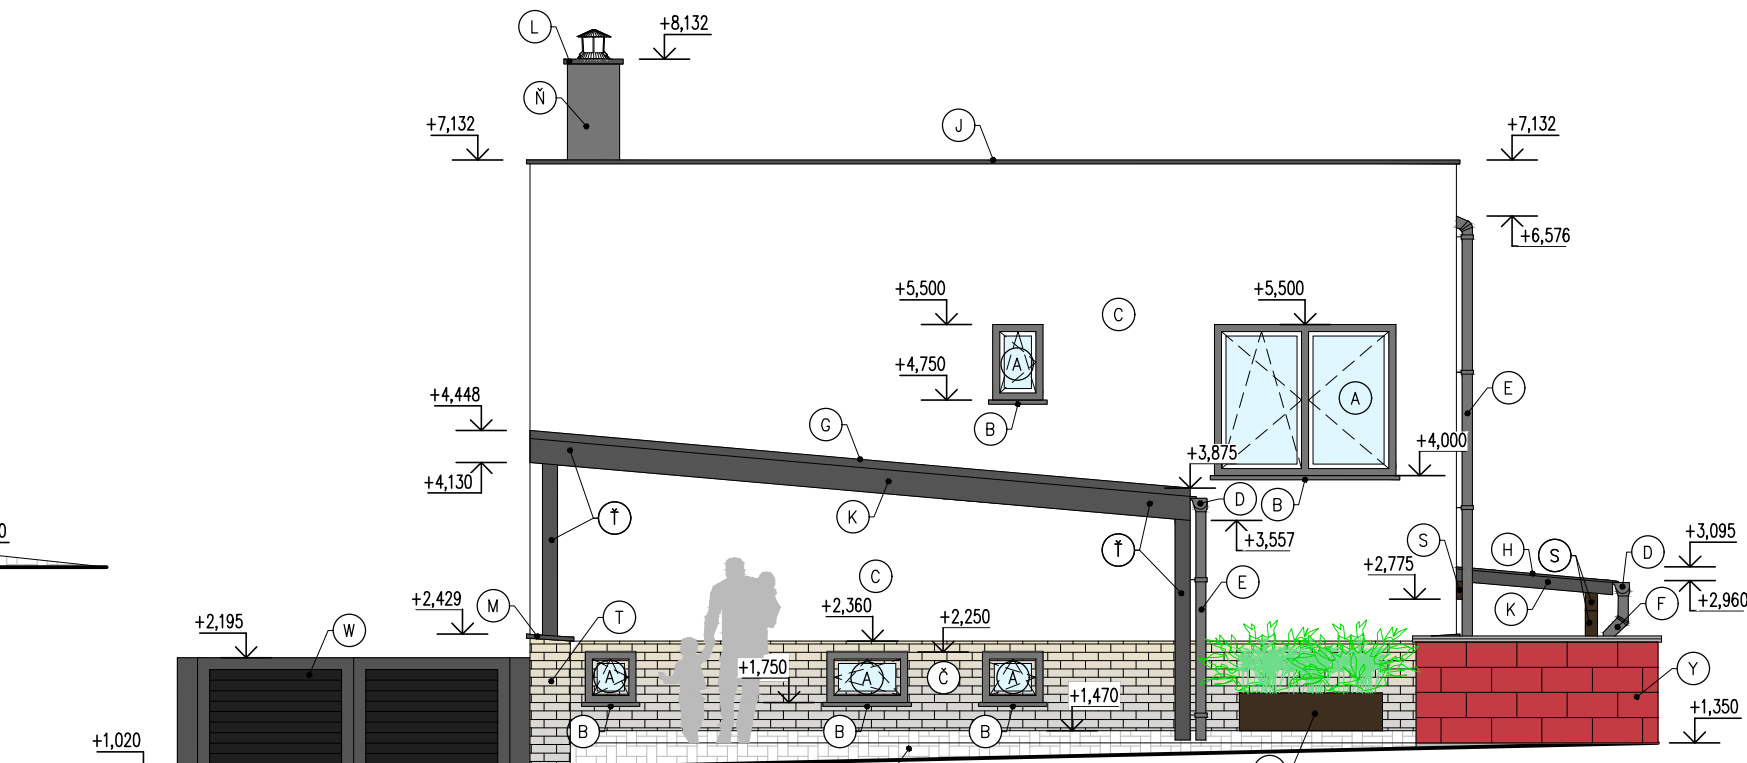

SEVEROVÝCHODNÝ POHĽAD

LEGENDA PRVKOV:

OZN.	DEFINOVANIE
A	FASÁDNE OTVOROVÉ PRVKY (OKNÁ, DVERE) Z PROFILOV NA BÁZE PVC-U A ZASKLENÉ IZOLAČNÝM 3-SKLÓM. (MATERIÁL A FARBU UPRESNÍ INVEŠTOR PRI REALIZÁCII)
B	KLAMPIARSKY VÝROBOK – VONKAJŠÍ ŤAHANÝ/POPLASTOVANÝ PARAPET (MATERIÁL A FARBU UPRESNÍ INVEŠTOR PRI REALIZÁCII)
C	FASÁDNÝ ZATEPLOVACÍ SYSTÉM: POVRCHOVÁ ÚPRAVA NA BÁZE SILIKÓNOVO-ZŤVIČNEJ FASÁDNEJ OMIETKY + TEPELNÁ IZOLÁCIA NA BÁZE FASÁDNEHO GRAFITOVÉHO (SIVÉHO) POLYSTYRÉNU hr.: 150 mm. (MATERIÁL A FARBU UPRESNÍ INVEŠTOR PRI REALIZÁCII)
Č	FASÁDNÝ ZATEPLOVACÍ SYSTÉM: POVRCHOVÁ ÚPRAVA NA BÁZE LEPENÉHO OBLKADU Z TRAVERTINOVÝCH TEHLÝCH PÁSIKOV + TEPELNÁ IZOLÁCIA NA BÁZE XPS hr.: 150/50 mm. (MATERIÁL A FARBU UPRESNÍ INVEŠTOR PRI REALIZÁCII)
D	ODKVAPOVÝ STREŠNÝ SYSTÉM: ODKVAPOVÝ POZINKOVANÝ/POPLASTOVANÝ POLKRUHOVÝ ŽĽAB 150. (MATERIÁL A FARBU UPRESNÍ INVEŠTOR PRI REALIZÁCII)
Ď	ODKVAPOVÝ STREŠNÝ SYSTÉM: ODKVAPOVÝ POZINKOVANÝ/POPLASTOVANÝ POLKRUHOVÝ ŽĽAB 100. (MATERIÁL A FARBU UPRESNÍ INVEŠTOR PRI REALIZÁCII)
E	ODKVAPOVÝ STREŠNÝ SYSTÉM: POZINKOVANÁ/POPLASTOVANÁ ZVODOVÁ RÚRA DN120. (MATERIÁL A FARBU UPRESNÍ INVEŠTOR PRI REALIZÁCII)
F	ODKVAPOVÝ STREŠNÝ SYSTÉM: POZINKOVANÁ/POPLASTOVANÁ ZVODOVÁ RÚRA DN80. (MATERIÁL A FARBU UPRESNÍ INVEŠTOR PRI REALIZÁCII)
G	STREŠNÁ KRYTINA: NOSNÝ TRAPÉZOVÝ PLECH (MATERIÁL A FARBU UPRESNÍ INVEŠTOR PRI REALIZÁCII)
H	STREŠNÁ KRYTINA: FALCOVANÁ PLECHOVÁ KRYTINA (MATERIÁL A FARBU UPRESNÍ INVEŠTOR PRI REALIZÁCII)
I	STREŠNÁ KRYTINA: PLNÉ POLYKARBONÁTOVÉ DOSKY (ALT. PLEXISKLO) (MATERIÁL A FARBU UPRESNÍ INVEŠTOR PRI REALIZÁCII)
J	KLAMPIARSKY VÝROBOK – OPLECHOVANIE ATIKY (POZINKOVANÝ/POPLASTOVANÝ PLECH) (MATERIÁL A FARBU UPRESNÍ INVEŠTOR PRI REALIZÁCII)
K	KLAMPIARSKY VÝROBOK – OPLECHOVANIE OBVODOVÉHO LEMOVANIA STRECHY (POZINKOVANÝ/POPLASTOVANÝ PLECH) (MATERIÁL A FARBU UPRESNÍ INVEŠTOR PRI REALIZÁCII)
L	KLAMPIARSKY VÝROBOK – OPLECHOVANIE KOMINOVÉHO TELESA (POZINKOVANÝ/POPLASTOVANÝ PLECH) (MATERIÁL A FARBU UPRESNÍ INVEŠTOR PRI REALIZÁCII)
M	KLAMPIARSKY VÝROBOK – OPLECHOVANIE OPORNEJ STENY (POZINKOVANÝ/POPLASTOVANÝ PLECH)(MATERIÁL A FARBU UPRESNÍ INVEŠTOR PRI REALIZÁCII)
N	EXTERIÉROVÉ ZÁBRADLIE: MONTOVANÉ Z PROFILOV NA BÁZE ZLIATIN HLINÍKA (MATERIÁL A FARBU UPRESNÍ INVEŠTOR PRI REALIZÁCII)
Ň	KOMINOVÉ TELESO: JEDNOPRIEDUCHOVÝ KOMÍN SCHIEDEL ZATEPELNÝ MINERÁLNOU VLNOU hr.: 80 mm + NEREZOVÁ KOMINOVÁ STRIEŠKA
O	DREVENÉ VERTIKÁLNE OTOČNÉ LAMELY OPATRENÉ VHODNÝM NÁTEROM DO EXTERIÉRU (MATERIÁL A FARBU UPRESNÍ INVEŠTOR PRI REALIZÁCII)
P	EXTERIÉROVÉ SCHODY: ŽELEZOBETONOVÁ KONŠTRUKCIA OPATRENÁ EPOXIDOVÝM NÁTEROM. (MATERIÁL A FARBU UPRESNÍ INVEŠTOR PRI REALIZÁCII)
Q	EXTERIÉROVÉ SCHODY: ŽELEZOBETONOVÁ KONŠTRUKCIA OPATRENÁ DREVENÝM OBLKADOM. (MATERIÁL A FARBU UPRESNÍ INVEŠTOR PRI REALIZÁCII)
R	DREVENÝ ZÁHRADNÝ KVETINÁČ S OKRASNÝMI RASTLINAMI/KRÍKMI
S	PRIZNANÉ DREVENÉ PRVKY OPATRENÉ VHODNÝM NÁTEROM DO EXTERIÉRU: STĽP + VÁŽNICA (MATERIÁL A FARBU UPRESNÍ INVEŠTOR PRI REALIZÁCII)
Š	ODKVAPOVÝ CHODNÍK: VYMÝVANÝ OKRASNÝ ŠTRK FRKACIE 8-16 mm A BETÓNOVÝ OBRUBNÍK. (MATERIÁL A FARBU UPRESNÍ INVEŠTOR PRI REALIZÁCII)
T	OPORNÁ STENA: ŽELEZOBETONOVÁ KONŠTRUKCIA Z BETÓNOVÝCH DT TVÁRNIC + TEPELNÁ IZOLÁCIA NA BÁZE XPS hr.: 50 mm.
ť	PRISTREŠOK PRE AUTÁ: OCELOVÉ PROFILY OPATRENÉ VHODNÝM NÁTEROM DO EXTERIÉRU. (MATERIÁL A FARBU UPRESNÍ INVEŠTOR PRI REALIZÁCII)
U	CHODNÍK ZHOTOVENÝ ZO ZÁMKOVEJ DLAŽBY S BETÓNOVÝMI OBRUBNÍKMI A PODKLADNÝMI VRSTVAMI (FARBU UPRESNÍ INVEŠTOR PRI REALIZÁCII)
V	SPEVNEŇA PLOCHA: STÁTIE A PRÍJAZD DO DVORA PRE AUTO ZHOTOVENÝ ZO ZÁMKOVEJ DLAŽBY S BETÓNOVÝMI OBRUBNÍKMI A PODKLADNÝMI VRSTVAMI (FARBU UPRESNÍ INVEŠTOR PRI REALIZÁCII)
W	DVOJKRIDLOVÁ BRÁNA PRE AUTO: HLINÍKOVÉ PROFILY OPATRENÉ VHODNÝM NÁTEROM DO EXTERIÉRU. (MATERIÁL A FARBU UPRESNÍ INVEŠTOR PRI REALIZÁCII)
X	JEDNOKRIDLOVÁ BRÁNIČKA: HLINÍKOVÉ PROFILY OPATRENÉ VHODNÝM NÁTEROM DO EXTERIÉRU. (MATERIÁL A FARBU UPRESNÍ INVEŠTOR PRI REALIZÁCII)
Y	PLOTOVÁ KONŠTRUKCIA: PLOTOVÉ POHĽADOVÉ BETÓNOVÉ MUROVACIE TVÁRNICE. (MATERIÁL A FARBU UPRESNÍ INVEŠTOR PRI REALIZÁCII)
Z	PODLAHOVÁ KONŠTRUKCIA TERASY: TERASOVÉ DREVENÉ PODLAHOVÉ DOSKY. (MATERIÁL A FARBU UPRESNÍ INVEŠTOR PRI REALIZÁCII)

POZNÁMKY:

- DOKUMENTÁCIA JE VYHOTOVENÁ V STUPNI PRE STAVEBNÝ ZÁMER A NENAHRAĐZA REALIZAČNÚ PROJEKTOVÚ DOKUMENTÁCIU.
- VÝŠKOVÉ KÓTY SA VZŤAHUJÚ KU KÓTE ±0,000 (MÔŽE BYŤ DODATOČNE UPRAVENÁ PRI OSAĐENÍ OBJEKTU Z HĽADISKA TERÉNYCH ÚPRAV).
- PRI ZHOTOVŤOVANÍ KONŠTRUKCIÍ TREBA DODRŽAŤ ZOHLADNIŤ VŠETKY POŽIADAVKY JEDNOTLIVÝCH PROFESIÍ.
- ZHOTOVITEĽ STAVBY MUŠI PREŠTUDOVAŤ CELÚ PROJEKTOVÚ DOKUMENTÁCIU A V PRÍPADE ZISTENIA NEDOSTATKOV NA NE UPOZORNIŤ.
- PRI REALIZÁCII STAVBY JE POTREBNÉ DODRŽAŤ PLATNÉ VYHLÁŠKY A STN.
- VŠETKY ZMENY A ZÁSADY DO NOSNÝCH KONŠTRUKCIÍ ZREALIZOVAŤ IBA PO ODSÚHLASENÍ PROJEKTANTOM STATIKY.
- KONŠTRUKCIE KTORÉ NIE SÚ ZAZNAČENÉ VO VÝKRESOVEJ DOKUMENTÁCII SA BLIŽŠIE ŠPECIFIKUJÚ POČAS REALIZÁCIE.
- PRI VÝSTAVBE JE NUTNÉ DODRŽAŤ A POSTUPOVAŤ PODĽA TECHNICKÝCH PREDPISOV VÝROBCOU JEDNOTLIVÝCH MATERIÁLOV.
- PRED VYHOTOVENÍM VÝPLNÍ OTVOROV JEDNOTLIVÉ OTVORY ZAMERAŤ A UPRESNIŤ.

xxxxx_SZP_01_1111_S01_AS_007_POH_00		0,000 = 644,73 m.n.m.		 Ing. Ján Bandik Mokrá 141281, 029 44 Rabča IČO: 54492599 DIČ: 1122948751 mobil: 0903 553 365 e-mail: bandik-j.projekt@gmail.com		PARÉ:
PROJEKT: NOVOSTAVBA RODINNÉHO DOMU		INVEŠTOR: Tomáš Žilka, Nad školou č. 675/36, 029 43 Zubrohlava		PEČIATKA A PODPIS:		
AUTOR:	Ing. Ján Bandik	MIESTO STAVBY: obec Zubrohlava, k.ú. Zubrohlava,				
ZODPOVEDNÝ PROJEKTANT:	Ing. Ján Bandik	okres Námestovo, č. parcely CKN 1227/226, 1227/227				
VYPRACOVAL:	Ing. Ján Bandik	ČÍSLO ZÁKAZKY: 20250801				
DRUH DOKUMENTU:	ARCHITEKTONICKO-STAVEBNÉ RIŠENIE	STUPEŇ DOKUMENTÁCIE: PSP A SZP: DOKUMENTÁCIA PRE STAVEBNÝ ZÁMER				
NÁZOV VÝKRESU:	POHĽADY	MIERKA: 1:75	DÁTUM: 11.2025	FORMÁT: 297x1050	ČÍSLO VÝKRESU: D-07	