


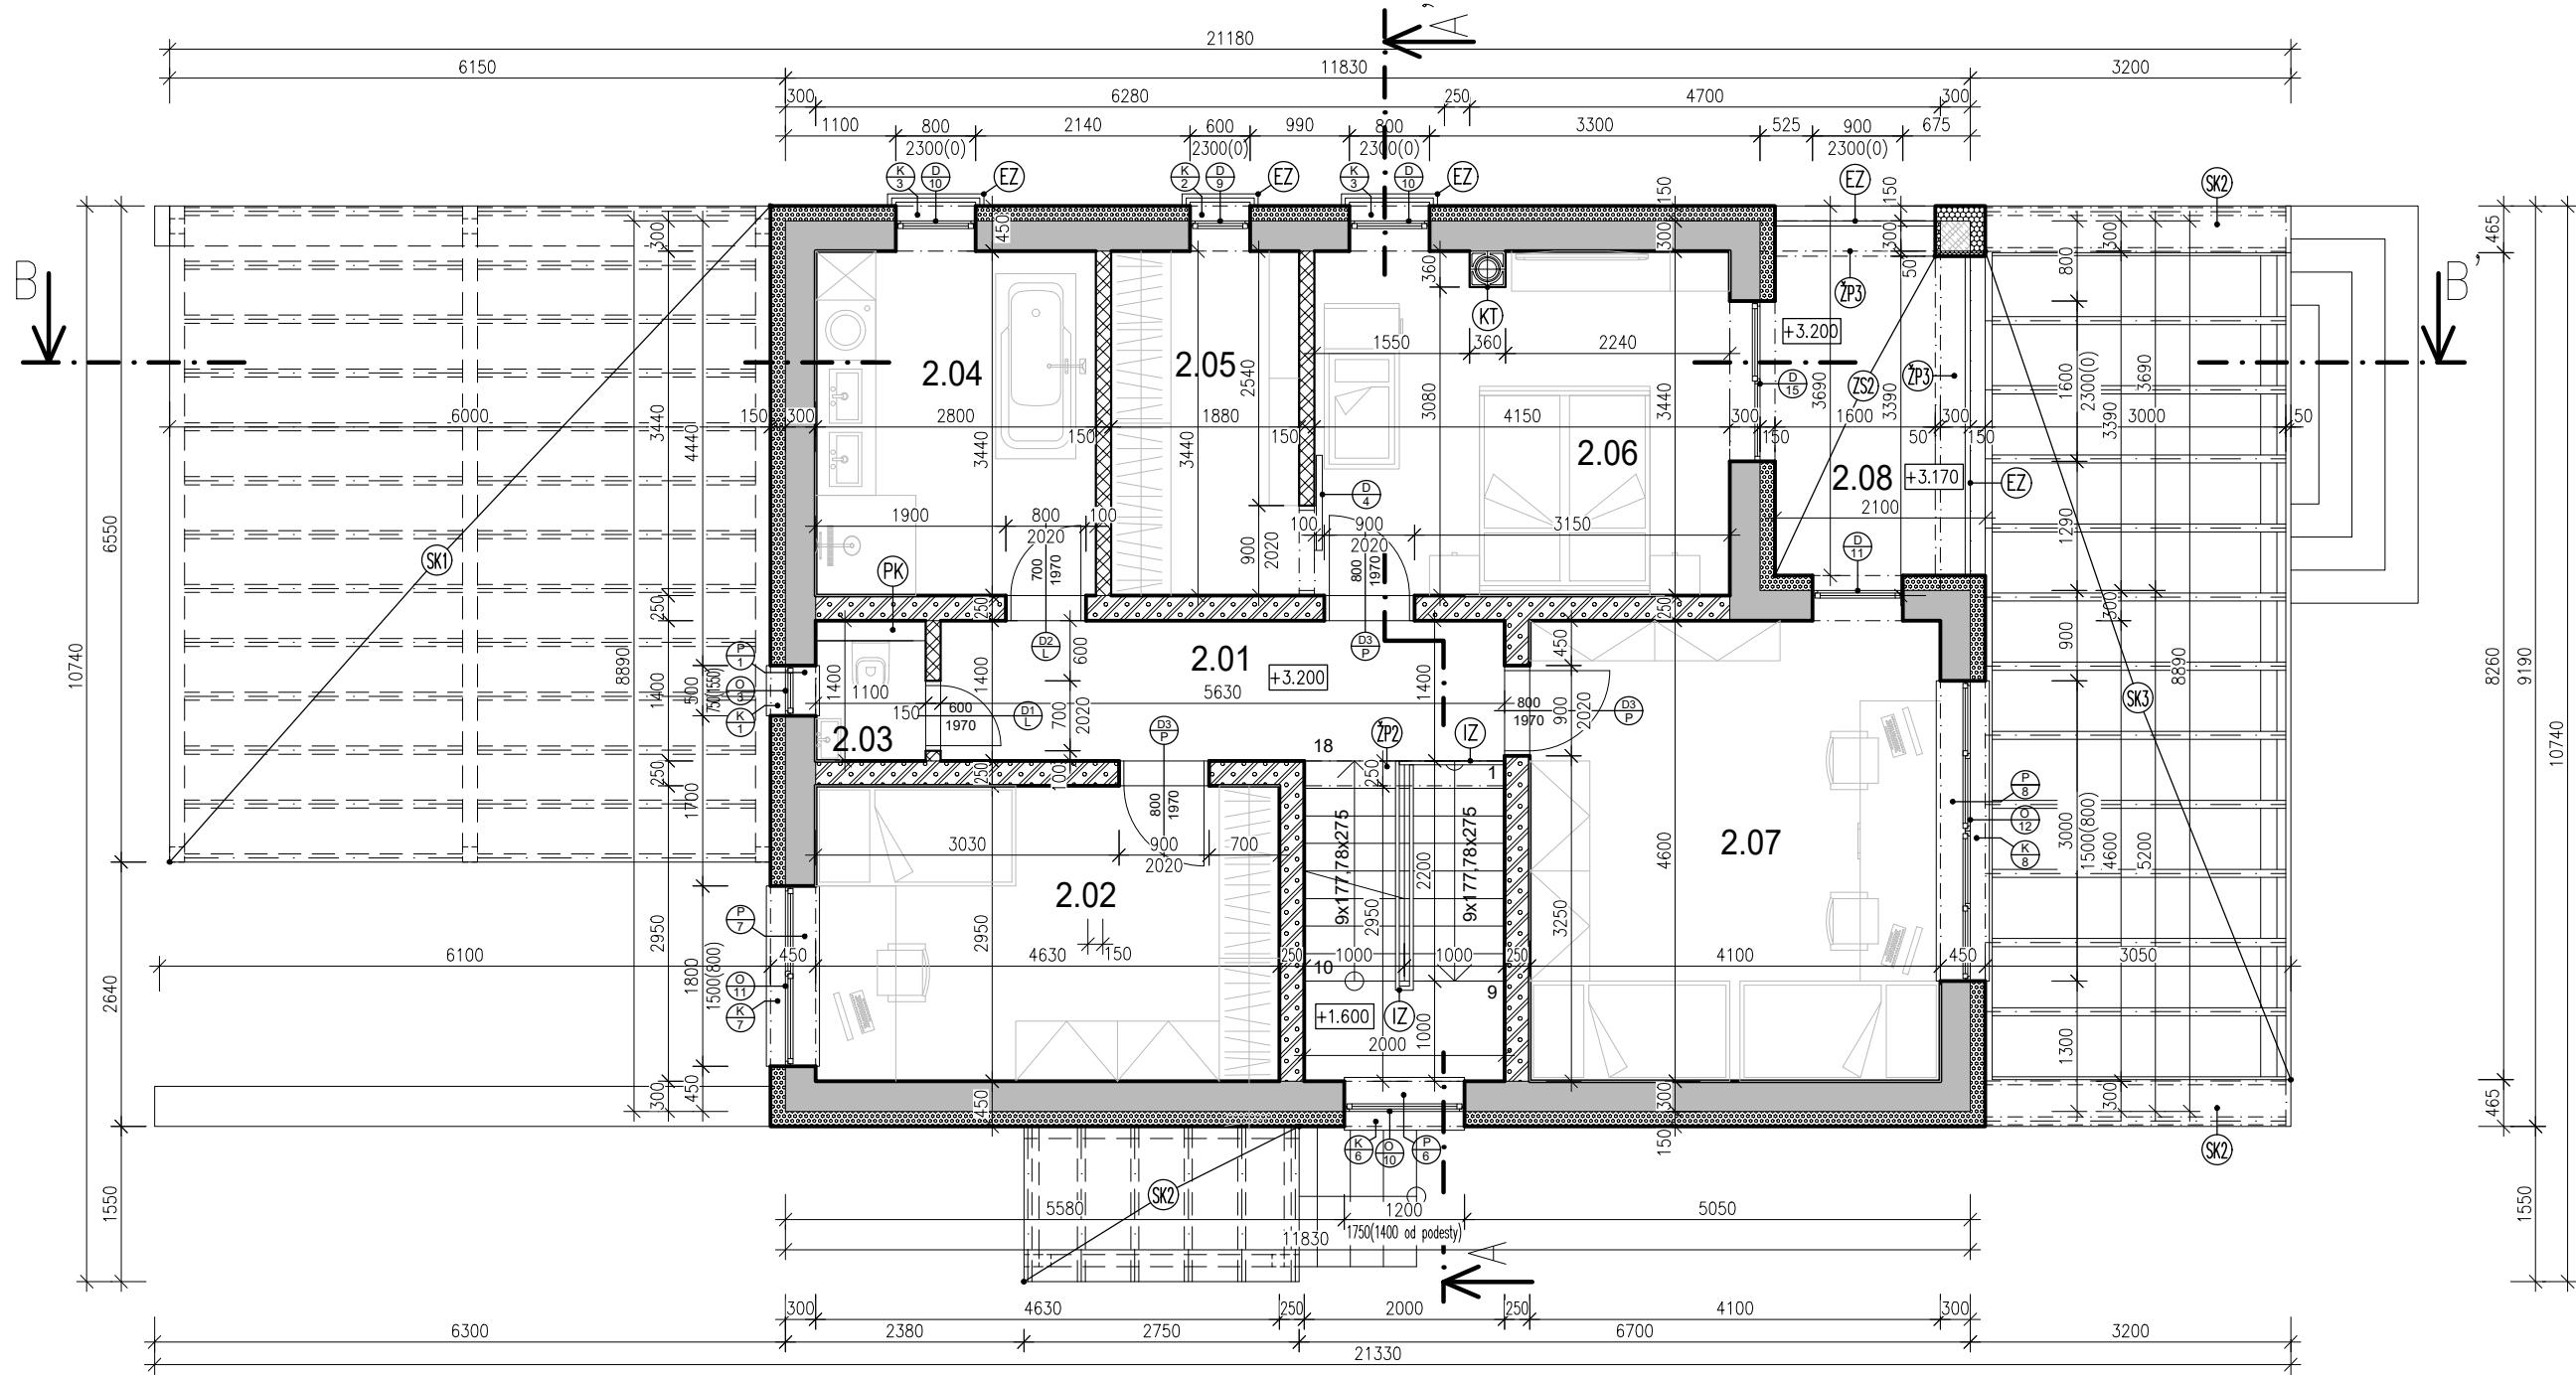

LEGENDA PRVKOV:

OZNAČ.	DEFINOVANIE	ŠPECIFIKÁCIA (mm)	POZNÁMKY
01–012	OZNAČENIE FASÁDNÝCH OKENNÝCH KONŠTRUKCIÍ	rozмеры podľa otvoru	hliníkový rám s izolačným 3–sklom
D1–D8	OZNAČENIE VNÚTORNÝCH DVERNÝCH KONŠTRUKCIÍ	rozмеры podľa otvoru	interiér. otváracé/posuvne drevené dvere s obložk. zárubňou
D9–D15	OZNAČENIE FASÁDNÝCH DVERNÝCH KONŠTRUKCIÍ	rozмеры podľa otvoru	hliníkový rám s izolačným 3–sklom
K1–K8	KLAMPIARSKÁ PRÁCA–VONKAJŠÍ PARAPET	rozмеры podľa otvoru	tahaný hliníkový parapet
P1–P8	VNÚTORNÝ PLASTOVÝ PARAPET	rozмеры podľa otvoru	komôrkový plastový parapet
IZ	VNÚTORNÉ SCHODISKOVÉ ZÁBRADLIE	do výšky 1000 mm	hliníkové profily kotvené do schodov a do steny
EZ	EXTERIÉROVÉ ZÁBRADLIE	do výšky 1000 mm	montované z hliníkových profilov
KT	KOMINOVÉ TELESO	360x360	jednoprieduchový systém schiedel
PK	PREDSTENOVÁ KONŠTRUKCIA WC	200x950x1200	geberit zabudovaný v predstenevej konštrukcii
ZS2	ZATEPLENIE STROPU NAD LODŽIOU	plocha: 1650x3240 mm	zateplenie ŽB stropu grafitovým EPS hr.: 150 mm
ŽP2	MONOLITICKÝ ŽELEZOBETÓNOVÝ PRIEVLAK TYP 2	prierez: 250x250 mm	(presnejšie vid. profesia statika)
ŽP3	MONOLITICKÝ ŽELEZOBETÓNOVÝ PRIEVLAK TYP 3	prierez: 250x350 mm	(presnejšie vid. profesia statika)
SK1	STREŠNÁ KRYTINA TYP 1	–	nosný trapézový plech
SK2	STREŠNÁ KRYTINA TYP 2	–	falcovaná plechová krytina
SK3	STREŠNÁ KRYTINA TYP 3	–	plné polykarbonátové dosky (alt. plexisklo)

POZNÁMKY:


- DOKUMENTÁCIA JE VYHOTOVENÁ V STUPNI PRE STAVEBNÝ ZÁMER A NENAHRÁDZA REALIZAČNÚ PROJEKTOVÚ DOKUMENTÁCIU.
- ROZMERY SÚ KÓTOVANÉ V SKLADOBNOM ROZMERE MUROVACIEHO PRVKU (BEZ TEPELNEJ IZOLÁCIE A OMIETOK / OBKLADOV).
- VÝŠKOVÉ KÓTY SA VZŤAHUJÚ KU KÓTE ±0.000 (MÔŽE BYŤ DODATOČNE UPRAVENÁ PRI OSADENÍ OBJEKTU Z HLADISKA TERÉNYCH ÚPRAV).
- PRI ZHOTOVOVANÍ KONŠTRUKCIÍ TREBA DODRŽAŤ VŠETKY POŽIADAVKY JEDNOTLIVÝCH PROFESIÍ (VYKUROVANIE, VODA, KANALIZÁCIA, ELEKTRINA) A ZABEZPEČIŤ POTREBNÉ VYTvoreNIE DRÁŽOK A PRESTUPOV CEZ JEDNOTLIVÉ KONŠTRUKCIE.
- ZHOTOVITEĽ STAVBY MUSÍ PREŠTUDOVAŤ CELÚ PROJEKTOVÚ DOKUMNETÁCIU A V PRÍPADE ZISTENIA NEDOSTATKOV NA NE UPOZORNIŤ.
- PRI REALIZÁCII STAVBY JE POTREBNÉ DODRŽAŤ PLATNÉ VYHLÁŠKY A STN.
- VŠETKY ZMENY A ZÁSAHY DO NOSNÝCH KONŠTRUKCIÍ ZREALIZOVAŤ IBA PO ODSÚHLASENÍ PROJEKTANTOM STATIKY.
- KONŠTRUKCIE, KTORÉ NIE SÚ ZAZNAČENÉ VO VÝKRESOVEJ DOKUMENTÁCI A SA BLIŽŠIE ŠPECIFIKUJÚ POČAS REALIZÁCIE.
- PRI VÝSTAVBE JE NUTNÉ DODRŽAŤ A POSTUPOVAŤ PODĽA TECHNICKÝCH PREDPISOV VÝROBCOU JEDNOTLIVÝCH MATERIÁLOV.
- PRED VYHOTOVENÍM VYPLNI OTVOROV JEDNOTLIVÉ OTVORY ZAMERAŤ A UPRESNIŤ.
- VŠETKY MUROVANÉ PRVKY KOTVIŤ K NOSNEJ KONŠTRUKCII POMOCOU MURIVOVEJ SPOJKY.
- NA NÁROŽIACH STIEN POUŽIŤ PODOMIETKOVÉ LIŠTY, UKONČENIA, NÁROŽIA KERAMICKÝCH OBKLADOV UKONČIŤ UKONČOVACÍMI PROFILMI.
- VNÚTORNÉ POVRCHY POD KERAMICKÝMI OBKLADMI OPATRIŤ TEKUTÝM HYDROIZOLAČNÝM NÁTEROM.

LEGENDA MIESTNOSTI 2.NP:

Č.M.	NÁZOV MIESTNOSTI	PLOCHA PODLAHY (m²)	VÝŠKA MIESTNOSTI (m)	POVRCHOVÁ ÚPRAVA				
				OZNAČENIE	DRUH PODLAHY	SOKEĽ	STENY	STROPY
2.01	CHODBA	7,88	2,600	P6	VINYLOVÁ PODLAHA	PODLAHOVÁ LIŠŤA	VÁPENNOCEMENT. OMIETKA	SADROKARTÓNOVÝ PODHLAD
2.02	DETSKÁ IZBA	13,66	2,600	P6	VINYLOVÁ PODLAHA	PODLAHOVÁ LIŠŤA	VÁPENNOCEMENT. OMIETKA	SADROKARTÓNOVÝ PODHLAD
2.03	WC	1,54	2,600	P5	KERAMICKÁ DLAŽBA	KERAMICKÝ SOKEĽ	KERAMICKÝ OBKLAD	SADROKARTÓNOVÝ PODHLAD
2.04	KÚPEĽŇA	9,63	2,600	P5	KERAMICKÁ DLAŽBA	KERAMICKÝ SOKEĽ	KERAMICKÝ OBKLAD	SADROKARTÓNOVÝ PODHLAD
2.05	ŠATNÍK	6,47	2,600	P6	VINYLOVÁ PODLAHA	PODLAHOVÁ LIŠŤA	VÁPENNOCEMENT. OMIETKA	SADROKARTÓNOVÝ PODHLAD
2.06	SPÁĽŇA	14,28	2,600	P6/P7	VINYLOVÁ PODLAHA	PODLAHOVÁ LIŠŤA	VÁPENNOCEMENT. OMIETKA	SADROKARTÓNOVÝ PODHLAD
2.07	DETSKÁ IZBA	18,86	2,600	P6	VINYLOVÁ PODLAHA	PODLAHOVÁ LIŠŤA	VÁPENNOCEMENT. OMIETKA	SADROKARTÓNOVÝ PODHLAD
2.08	LODŽIA	7,50	2,650	P8	MRAVZD. KERAM. DLAŽBA	KERAMICKÝ SOKEĽ	FASÁDNA OMIETKA	FASÁDNA OMIETKA
SPOLU PLOCHA		79,82						
				ÚŽITKOVÁ PLOCHA: 72,32 m²				
				OBYTNÁ PLOCHA: 46,80 m²				

LEGENDA MATERIÁLOV:

- OBVODOVÉ A VNÚTORNÉ NOSNÉ PÓROBETÓNOVÉ MURIVO TERMALICA 350 hr.: 300 mm, O ROZMEROCH: 599 x 249 x 300 mm (DxVxŠ), NA TENKOVRSŤVÚ LEPIACU MALTU
- VNÚTORNÉ NOSNÉ PÓROBETÓNOVÉ MURIVO PORFIX P2-440 hr.: 250 mm, O ROZMEROCH: 500 x 250 x 250 mm (DxVxŠ), NA TENKOVRSŤVÚ LEPIACU MALTU
- STĽPOVÉ BETÓNOVÉ DEBNIACE TVÁRNICE ST-25 hr.: 250 mm, O ROZMEROCH 250 x 250 x 250 mm (DxVxŠ), VYPLŇ: BETÓN tr.: 25/30 + OCEĽOVÁ VÝSTUŽ tr.: 10425
- VNÚTORNÉ NENOSNÉ PÓROBETÓNOVÉ MURIVO PORFIX P2-500 hr.: 150 mm, O ROZMEROCH - 500 x 250 x 150 mm (DxVxŠ), NA TENKOVRSŤVÚ LEPIACU MALTU
- FASÁDNY ZATEPLOVACÍ SYSTÉM TVORENÝ Z FASÁDNEJ TEPELNEJ IZOLÁCIE NA BÁZE GRAFITOVÉHO (SIVÉHO) EPS hr.: 150 mm A POVRCHOVOU ÚPRAVOU NA BÁZE SILIKÓNOVO-ZŽIVICNEJ FASÁDNEJ OMIETKY
- FASÁDNY ZATEPLOVACÍ SYSTÉM TVORENÝ Z FASÁDNEJ TEPELNEJ IZOLÁCIE NA BÁZE XPS hr.: 150 mm / 50 mm A POVRCHOVOU ÚPRAVOU NA BÁZE SILIKÓNOVO-ZŽIVICNEJ FASÁDNEJ OMIETKY

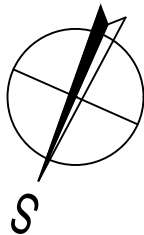

Ing. Ján Bandík
Mokrá 1412/61, 029 44 Rabča
IČO: 54492599 DiČ: 1122949751
mobil: 0903 553 365
e-mail: bandik.j.projekt@gmail.com

PARÉ:

PROJEKT: NOVOSTAVBA RODINNÉHO DOMU		INVESTOR: Tomáš Žilka, Nad školou č. 675/36, 029 43 Zubrohľava		PEČIATKA A PODPIS:	
AUTOR:	Ing. Ján Bandík	MIESTO STAVBY: obec Zubrohľava, k.ú. Zubrohľava, okres Námestovo, č. parcely CKN 1227/226, 1227/227			
ZODPOVEDNÝ PROJEKTANT:	Ing. Ján Bandík				
VYPRACOVAL:	Ing. Ján Bandík	ČÍSLO ZÁKAZKY: 20250801			
DRUH DOKUMENTU: ARCHITEKTONICKO-STAVEBNÉ RIEŠENIE		STUPEŇ DOKUMENTÁCIE: PSP A SZP: DOKUMENTÁCIA PRE STAVEBNÝ ZÁMER			
NÁZOV VÝKRESU: PÓDORYS 2.NP		MIERKA: 1:75	DÁTUM: 11.2025		FORMÁT: 297x630